02

設計相關檢討

2-1　平面圖
2-2　立面圖
2-3　剖面圖
2-4　地面景觀配置圖
2-5　夜間照明計畫
2-6　透視圖

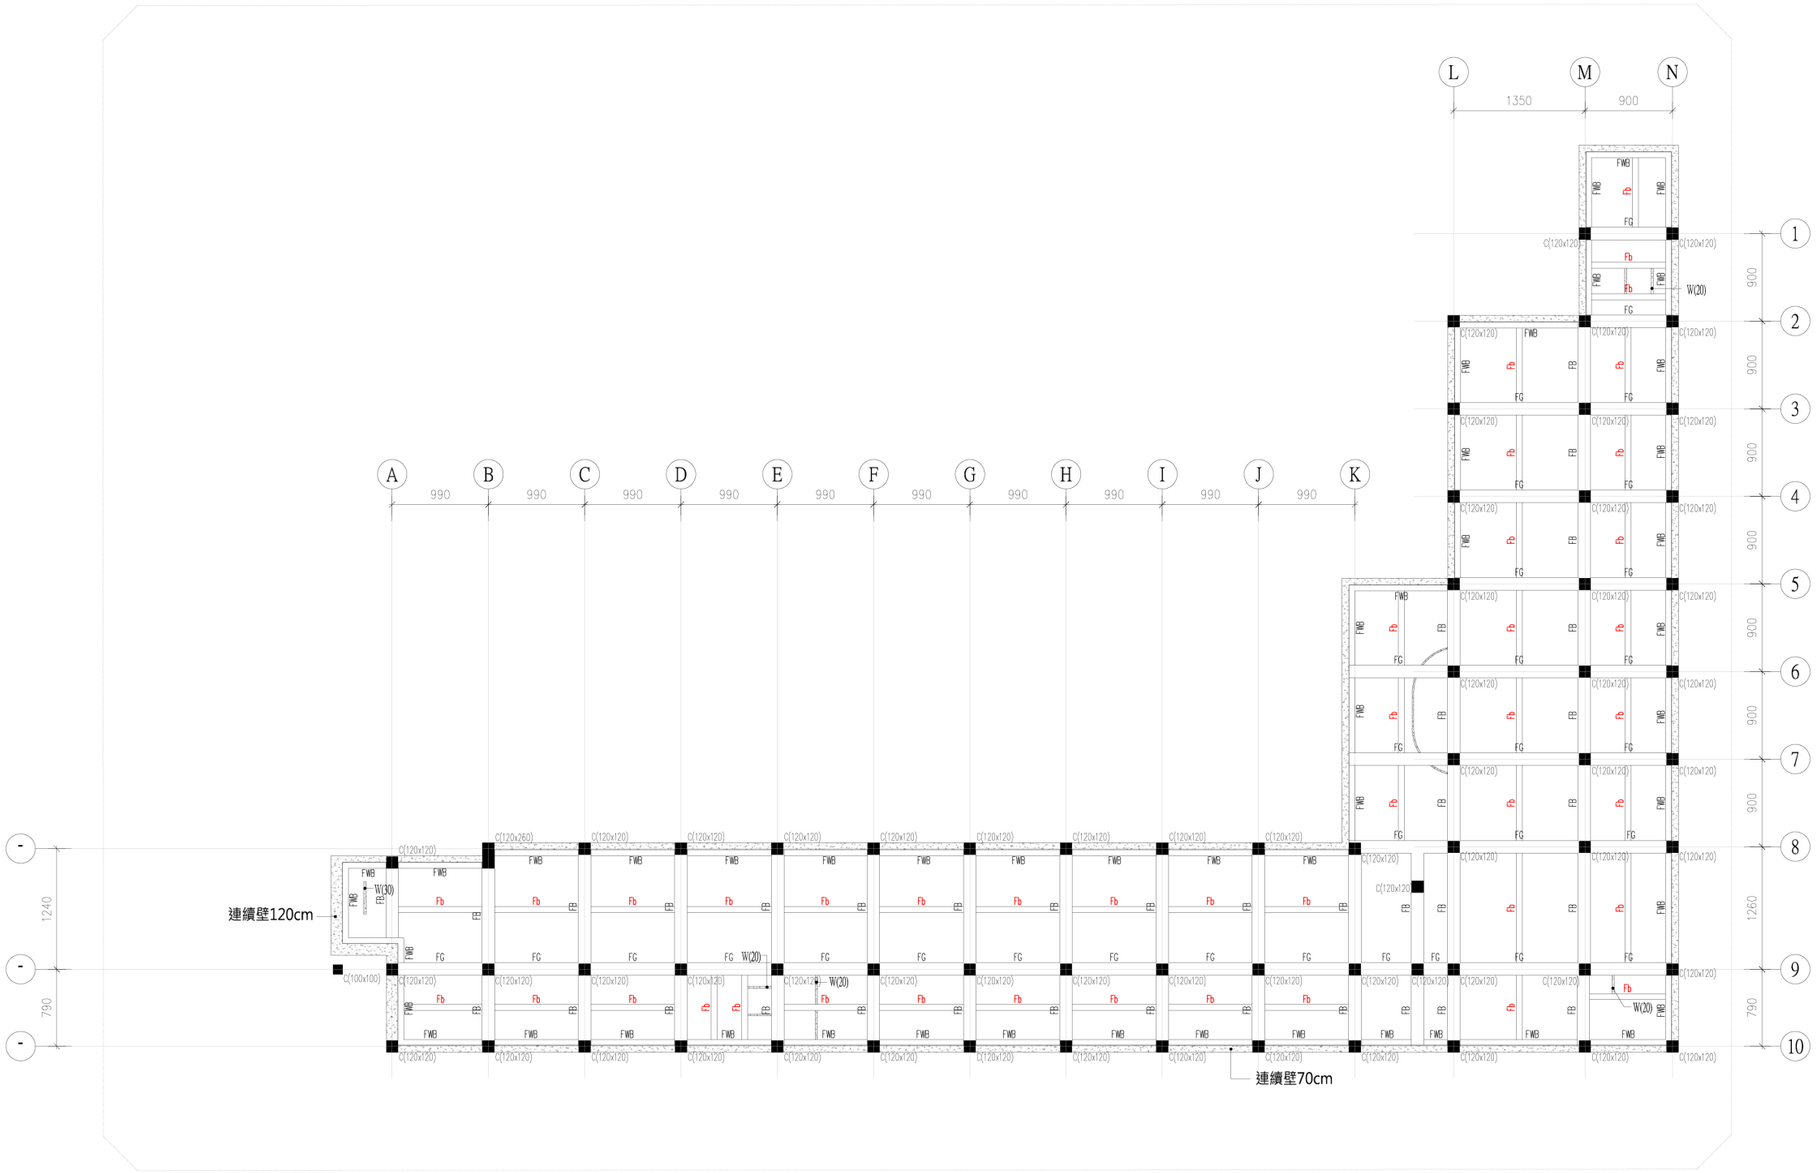

筏基層平面圖

0 6 12 24m

N

2-1 平面圖

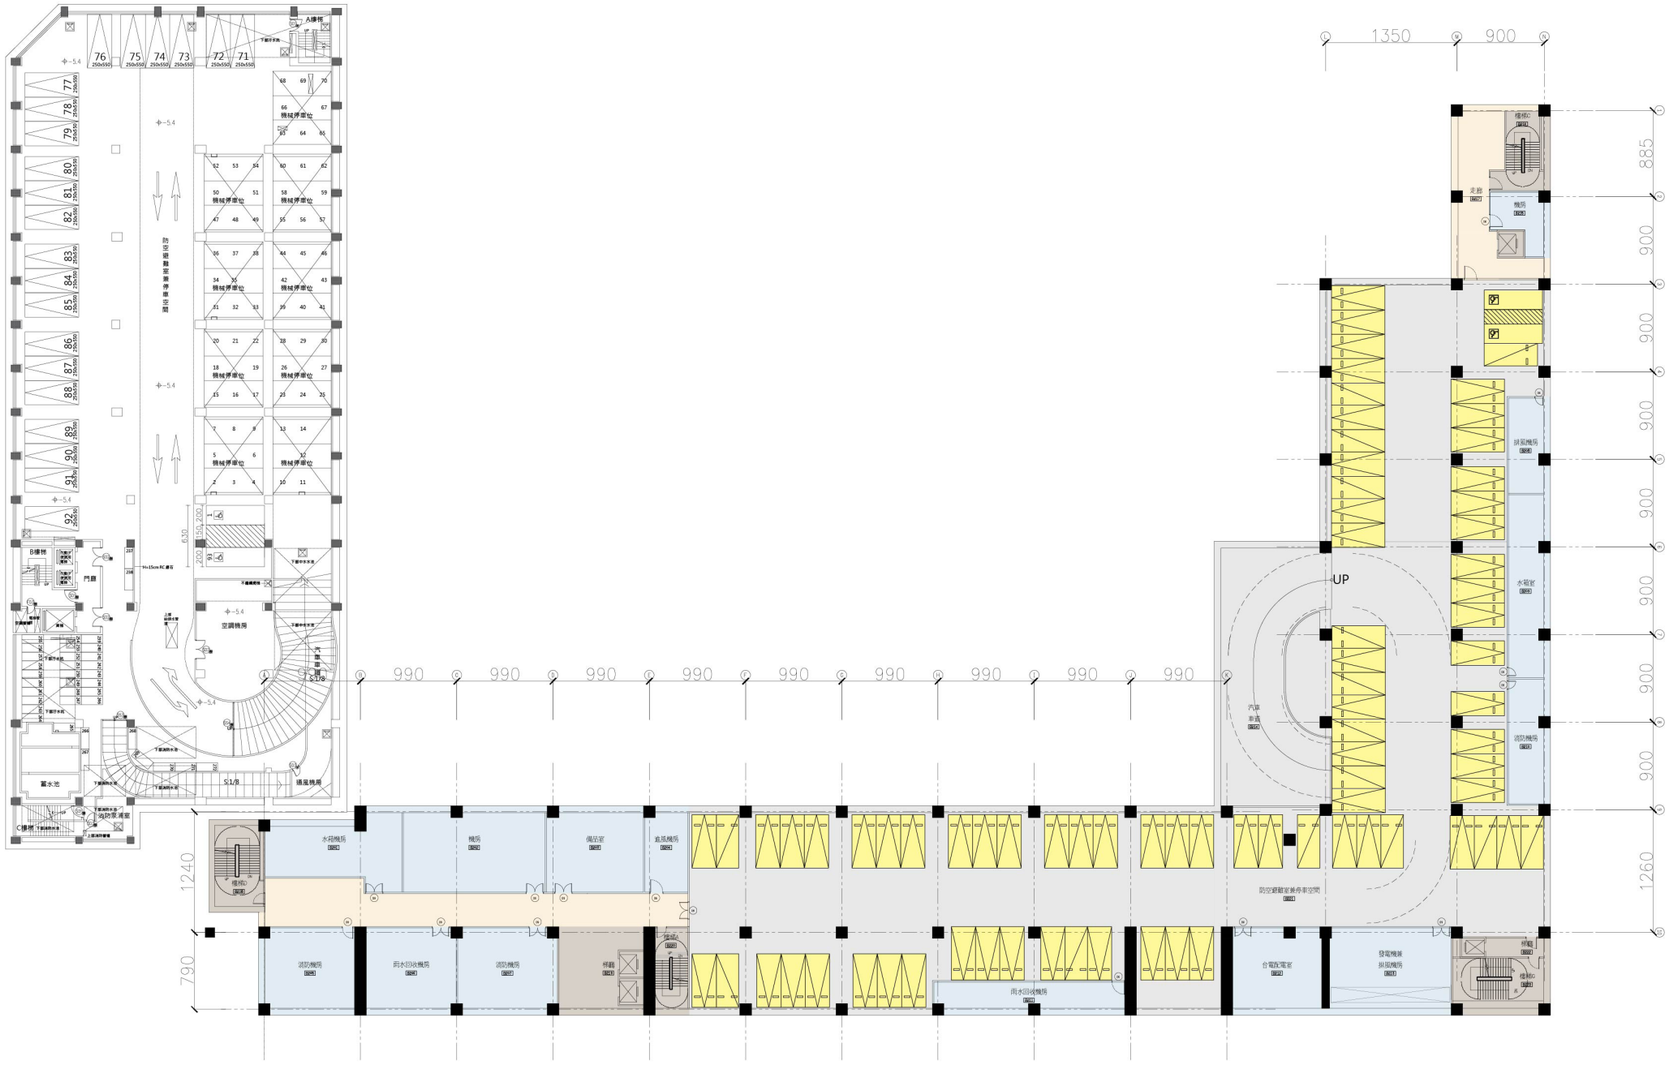

地下二層平面圖

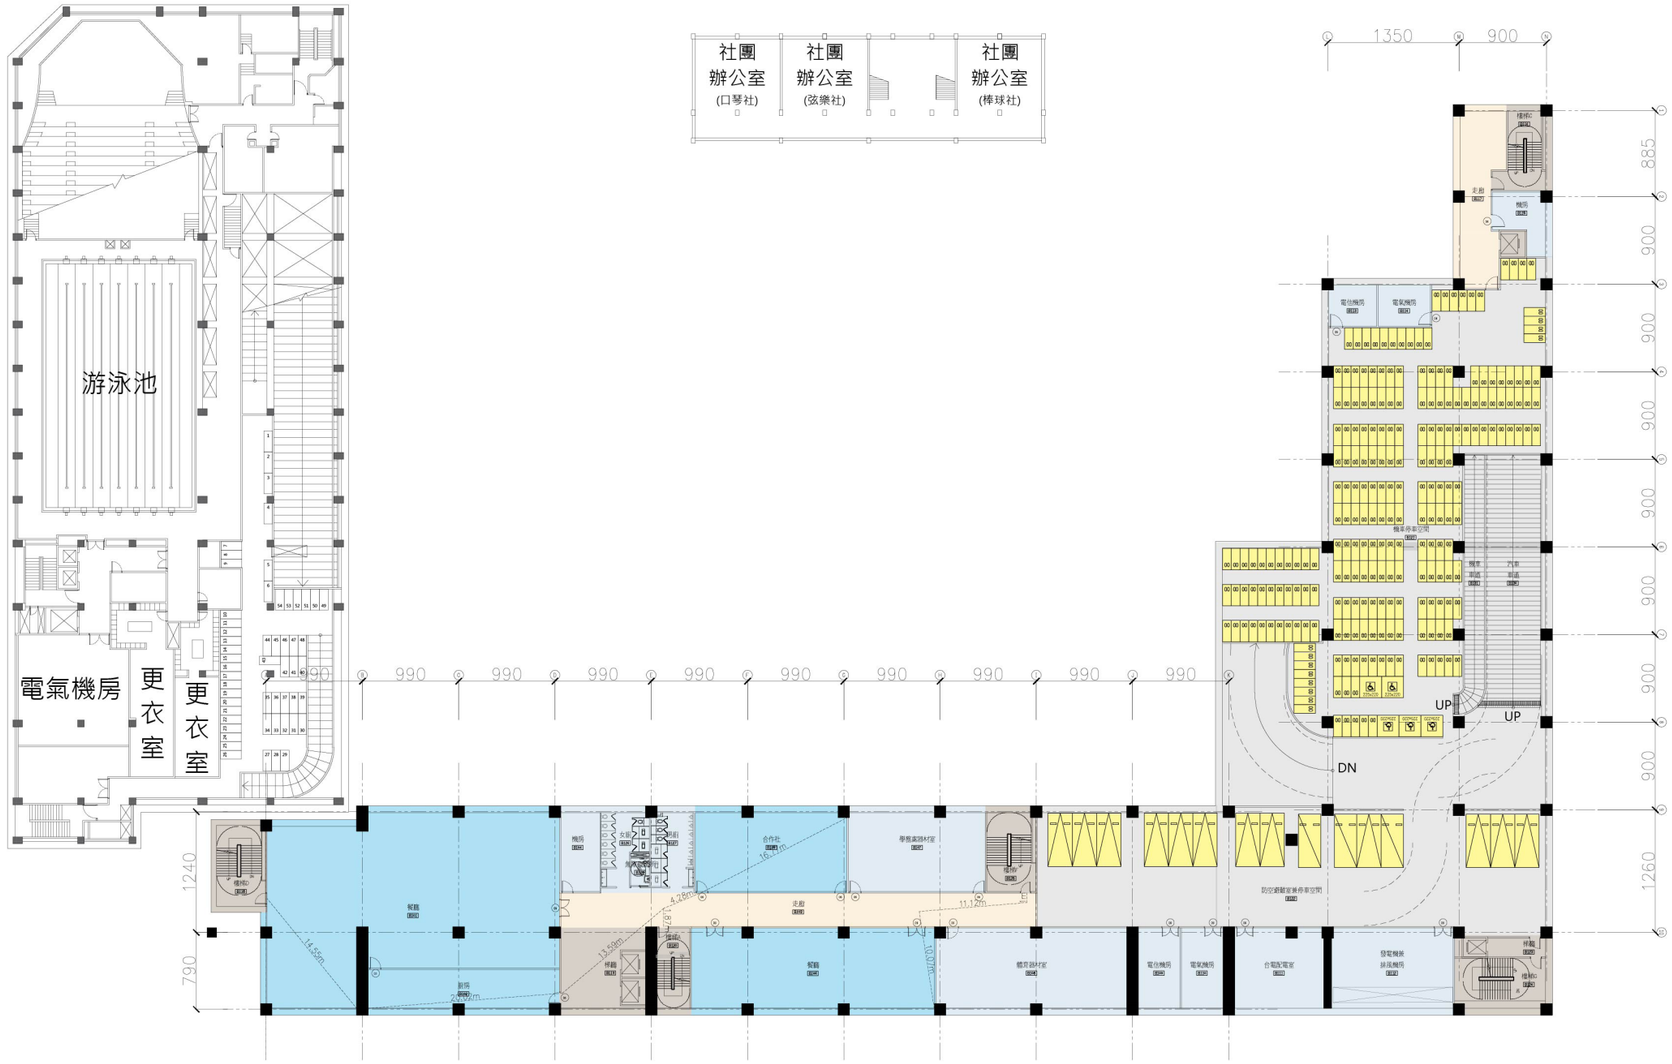

地下一層平面圖

0 6 12 24m

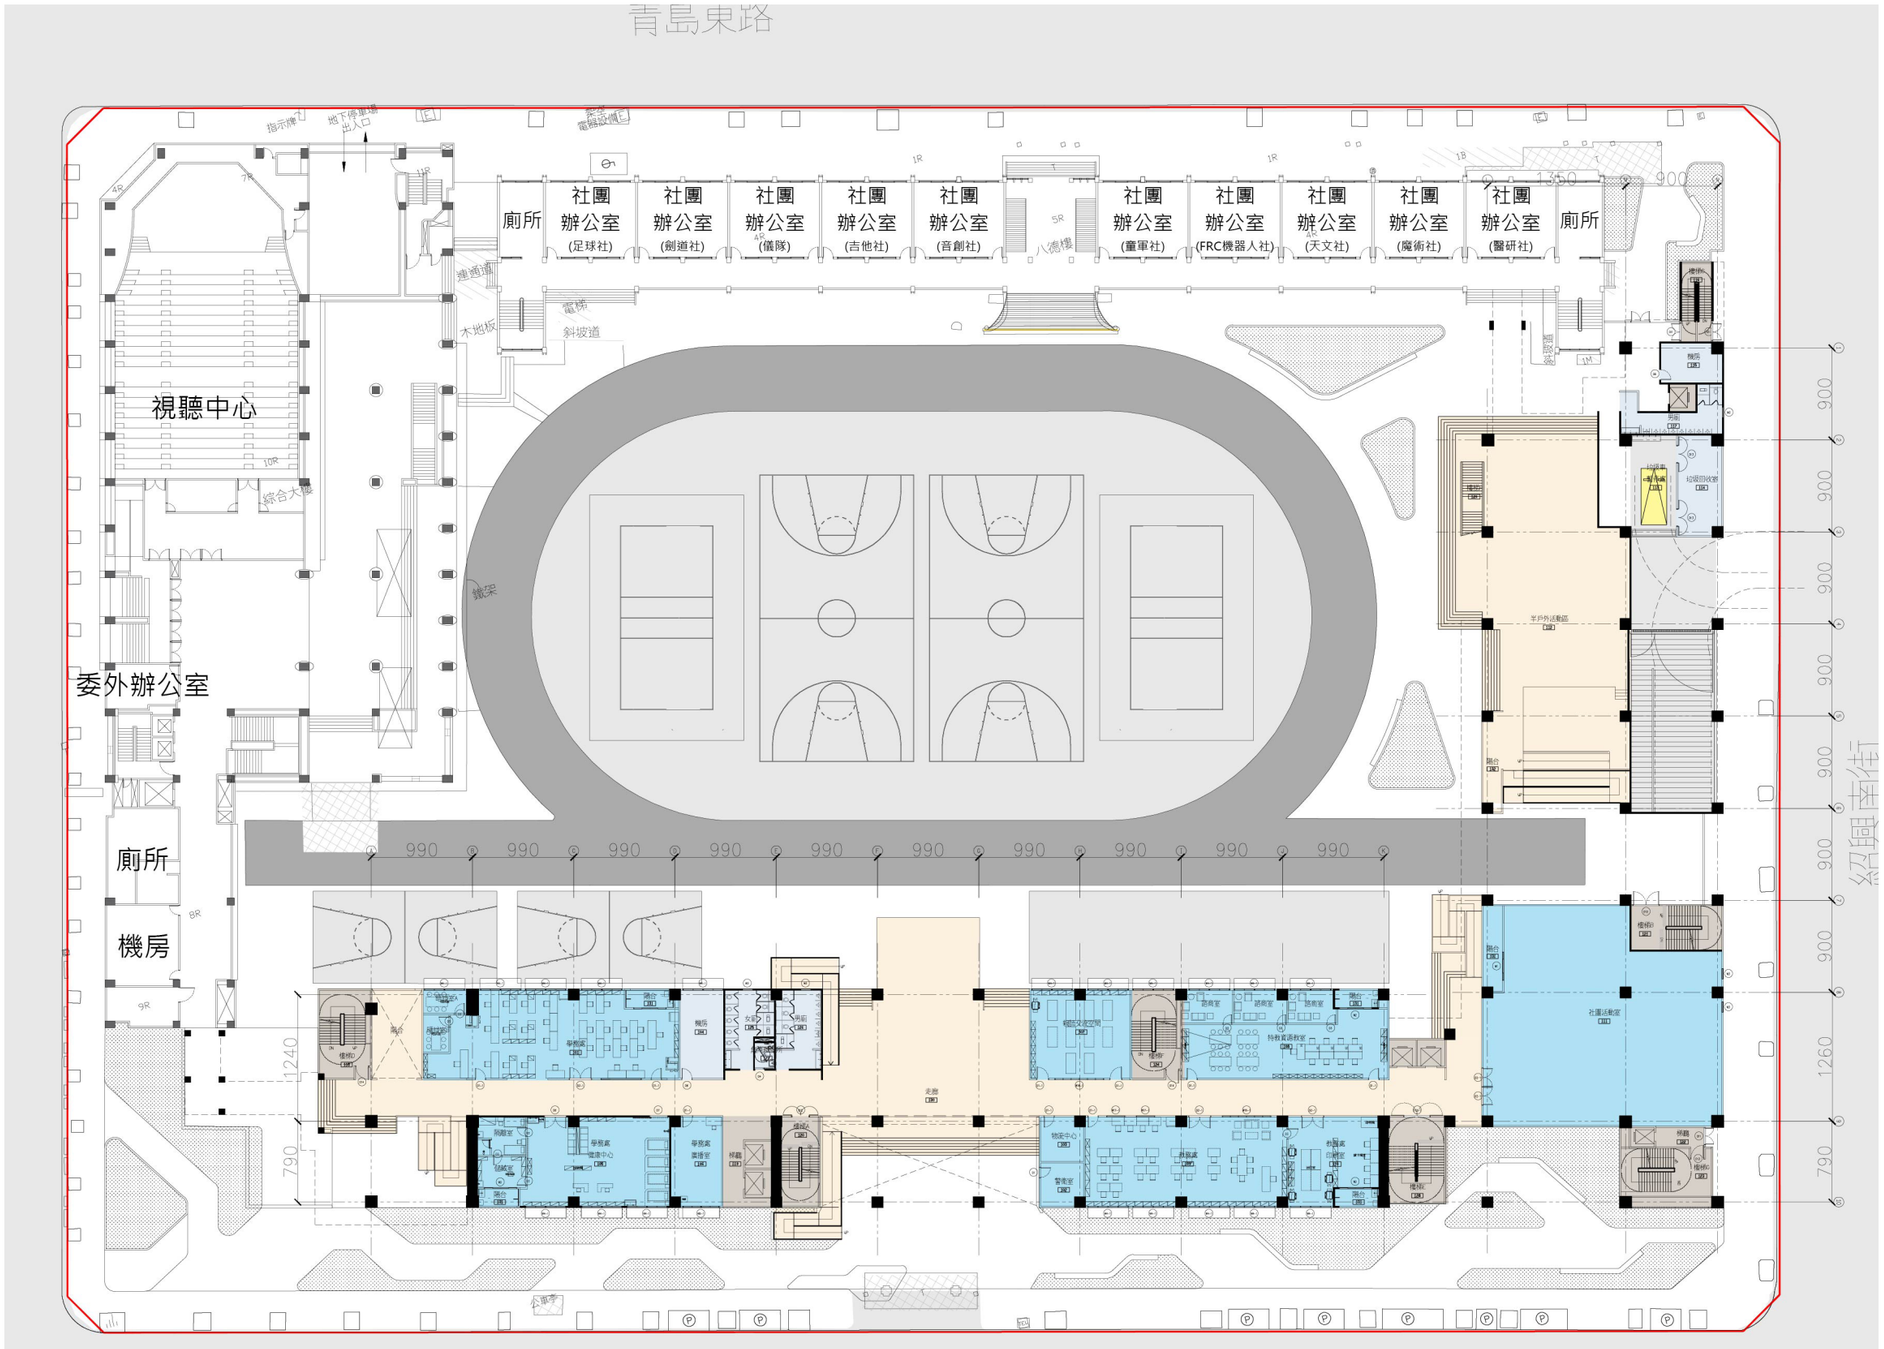

一層平面圖

0 6 12 24m

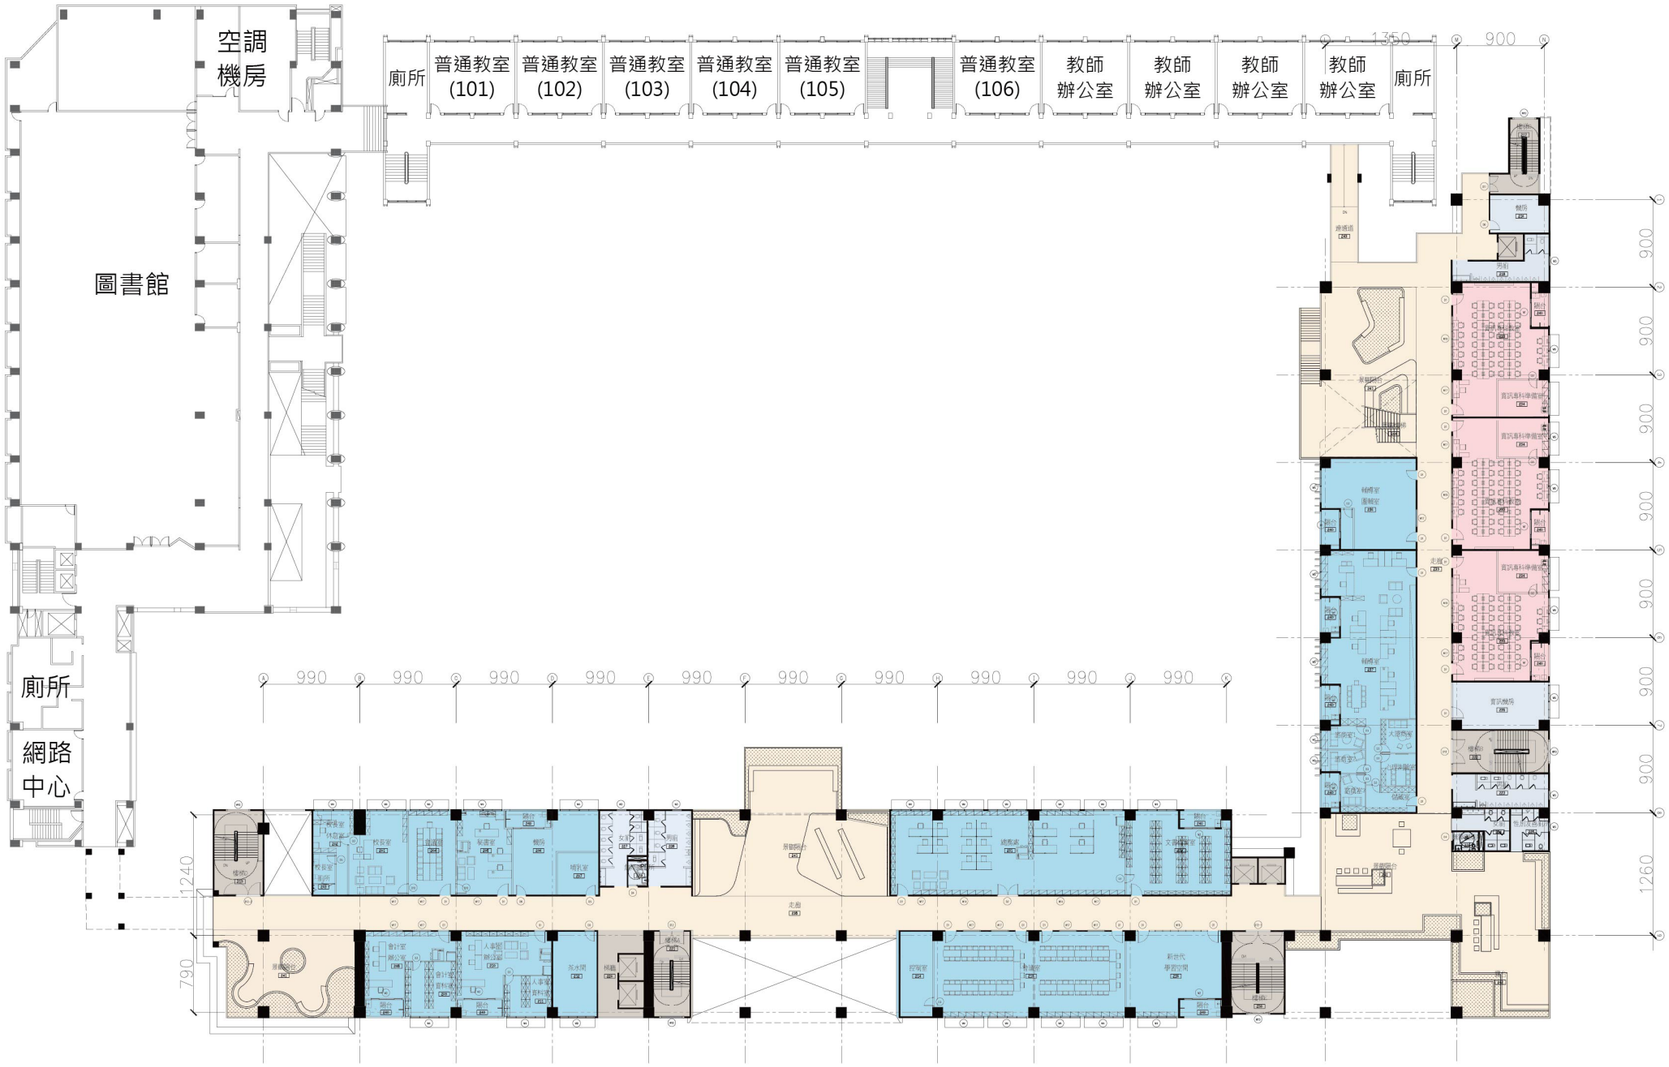

二層平面圖

0 6 12 24m

N

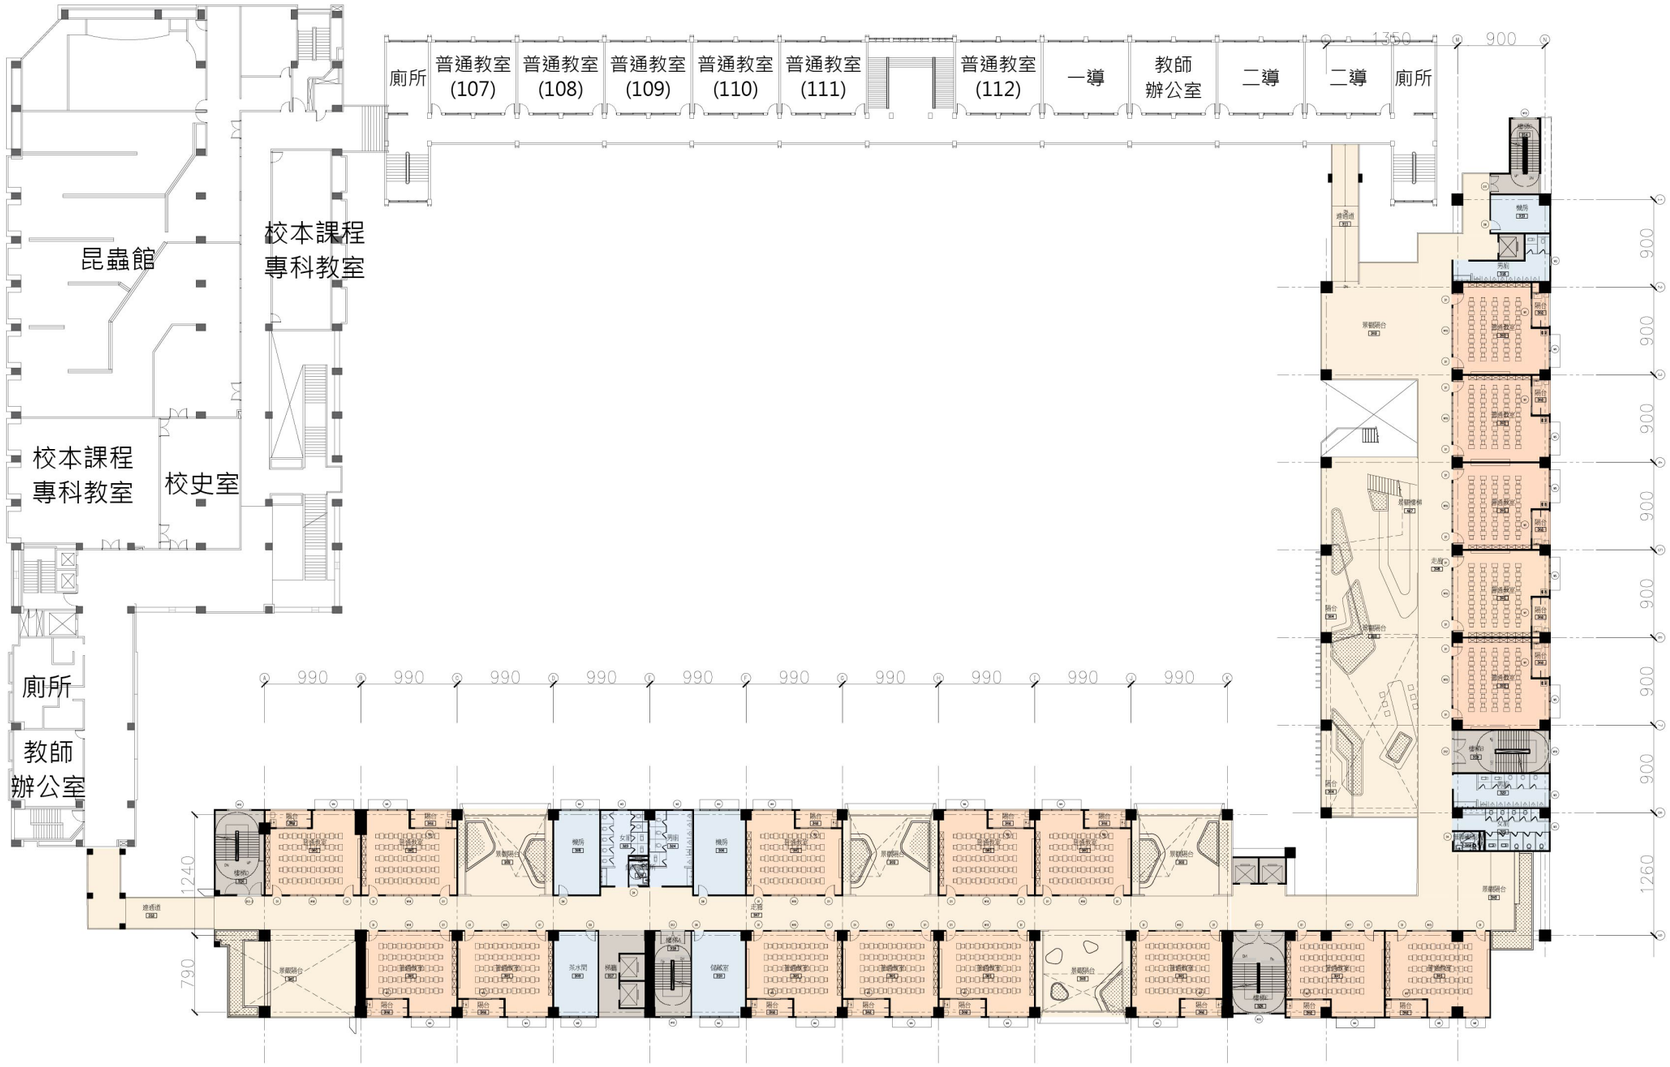

三層平面圖

0 6 12 24m

N

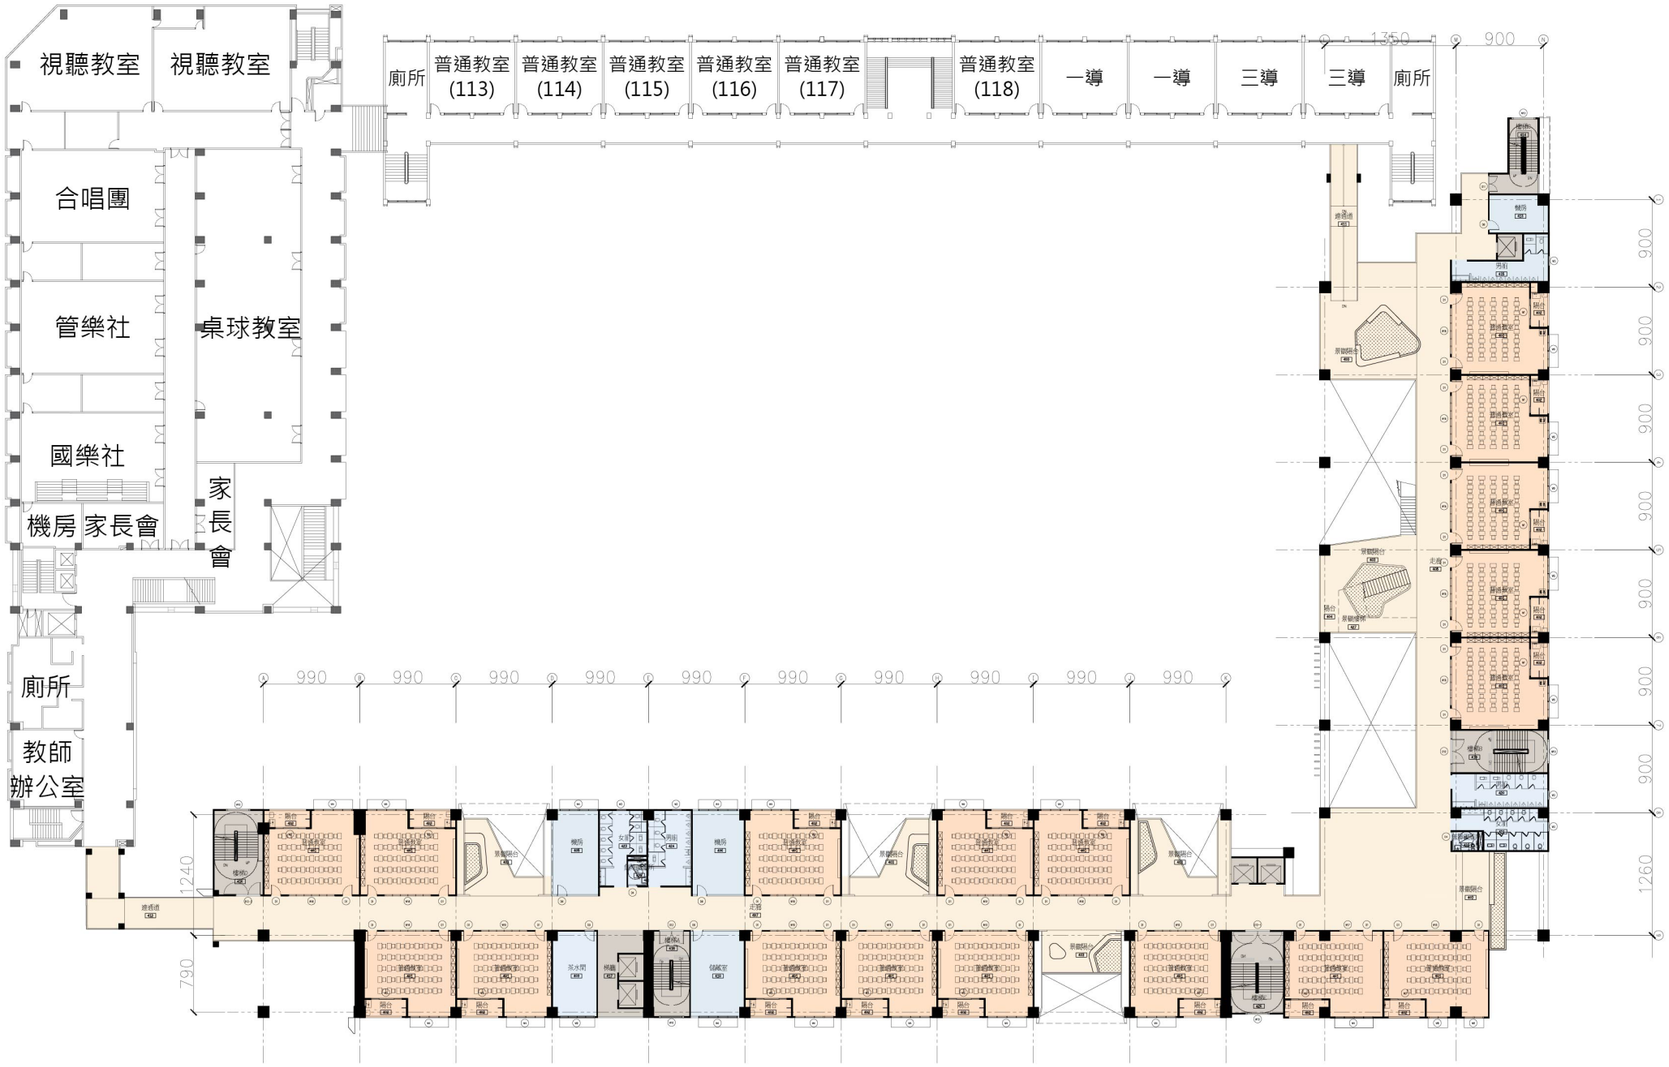

四層平面圖

0 6 12 24m

N

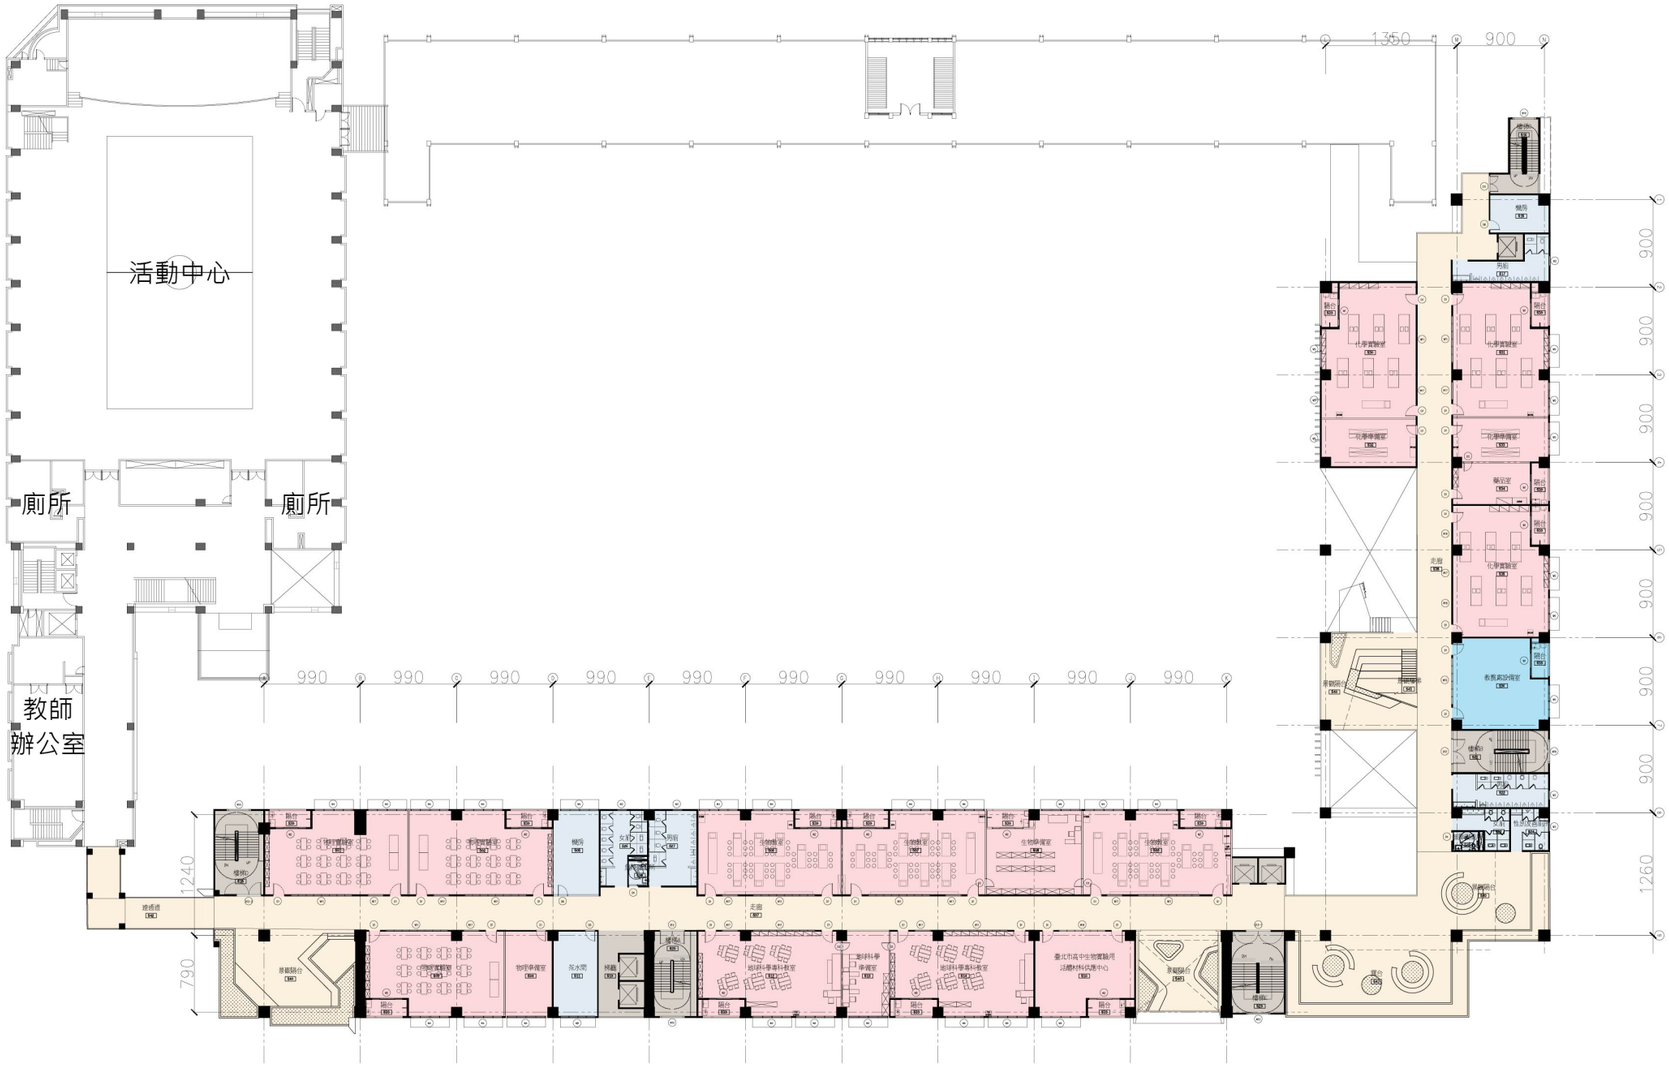

五層平面圖

0 6 12 24m

N

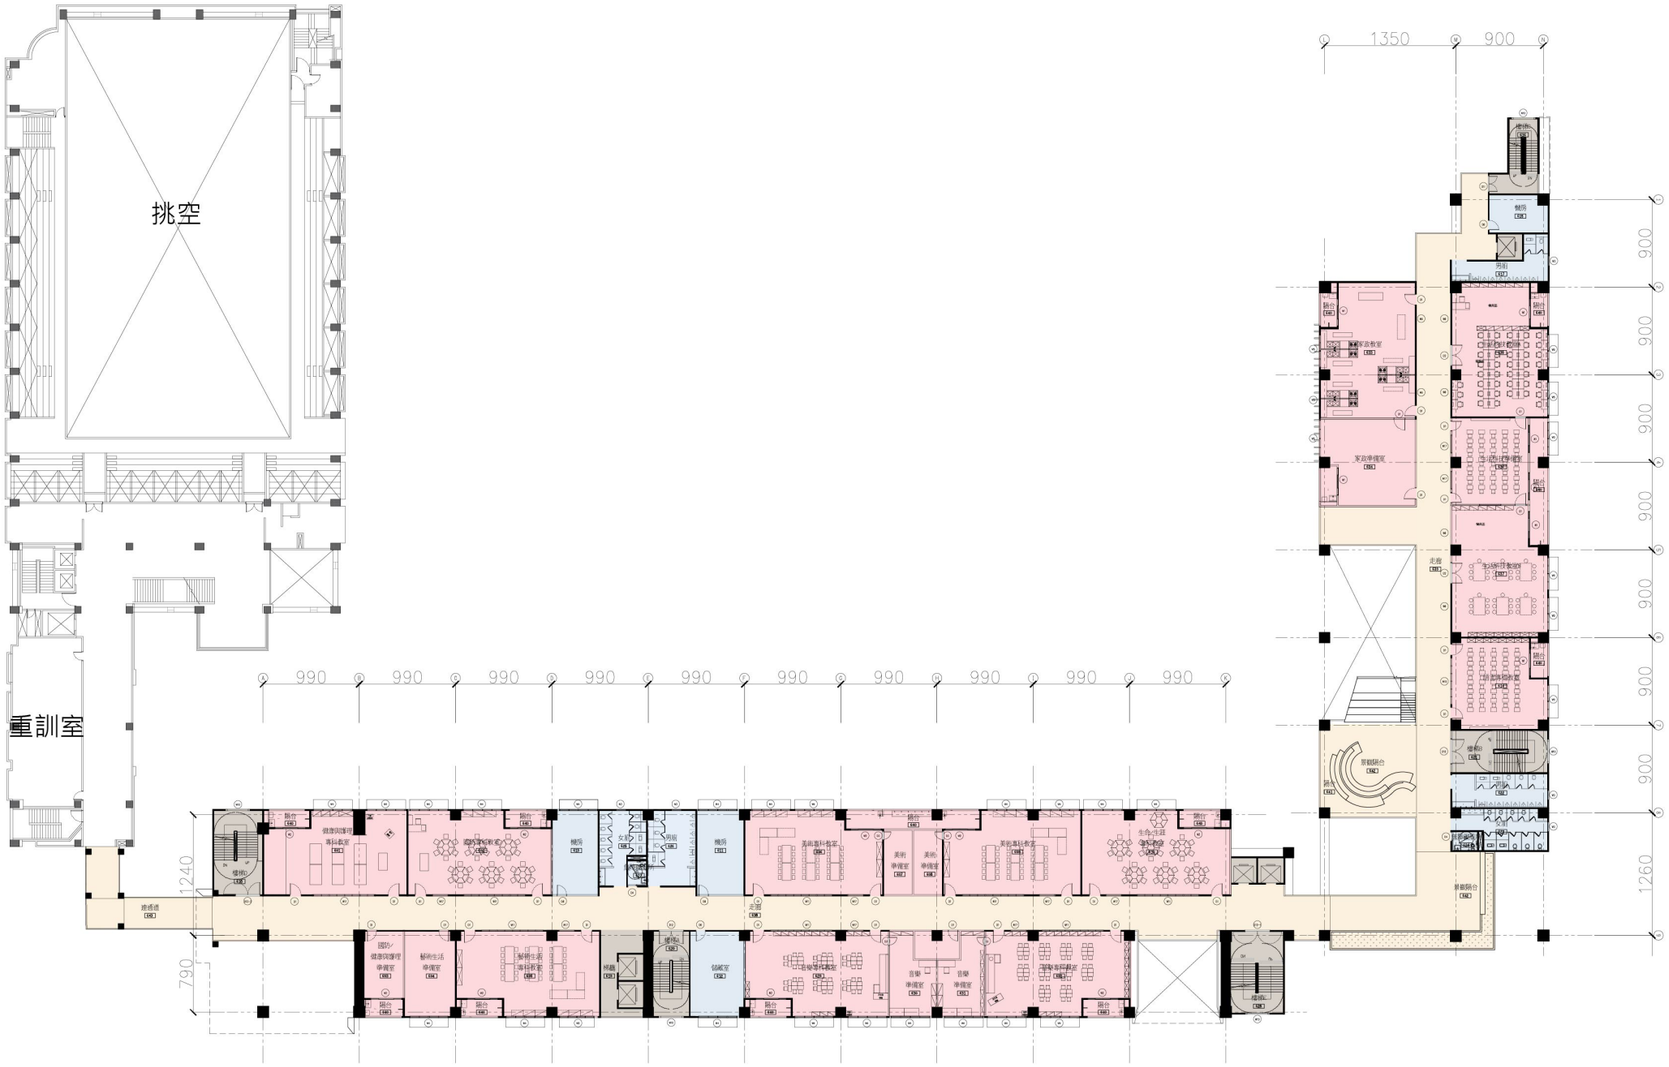

六層平面圖

0 6 12 24m